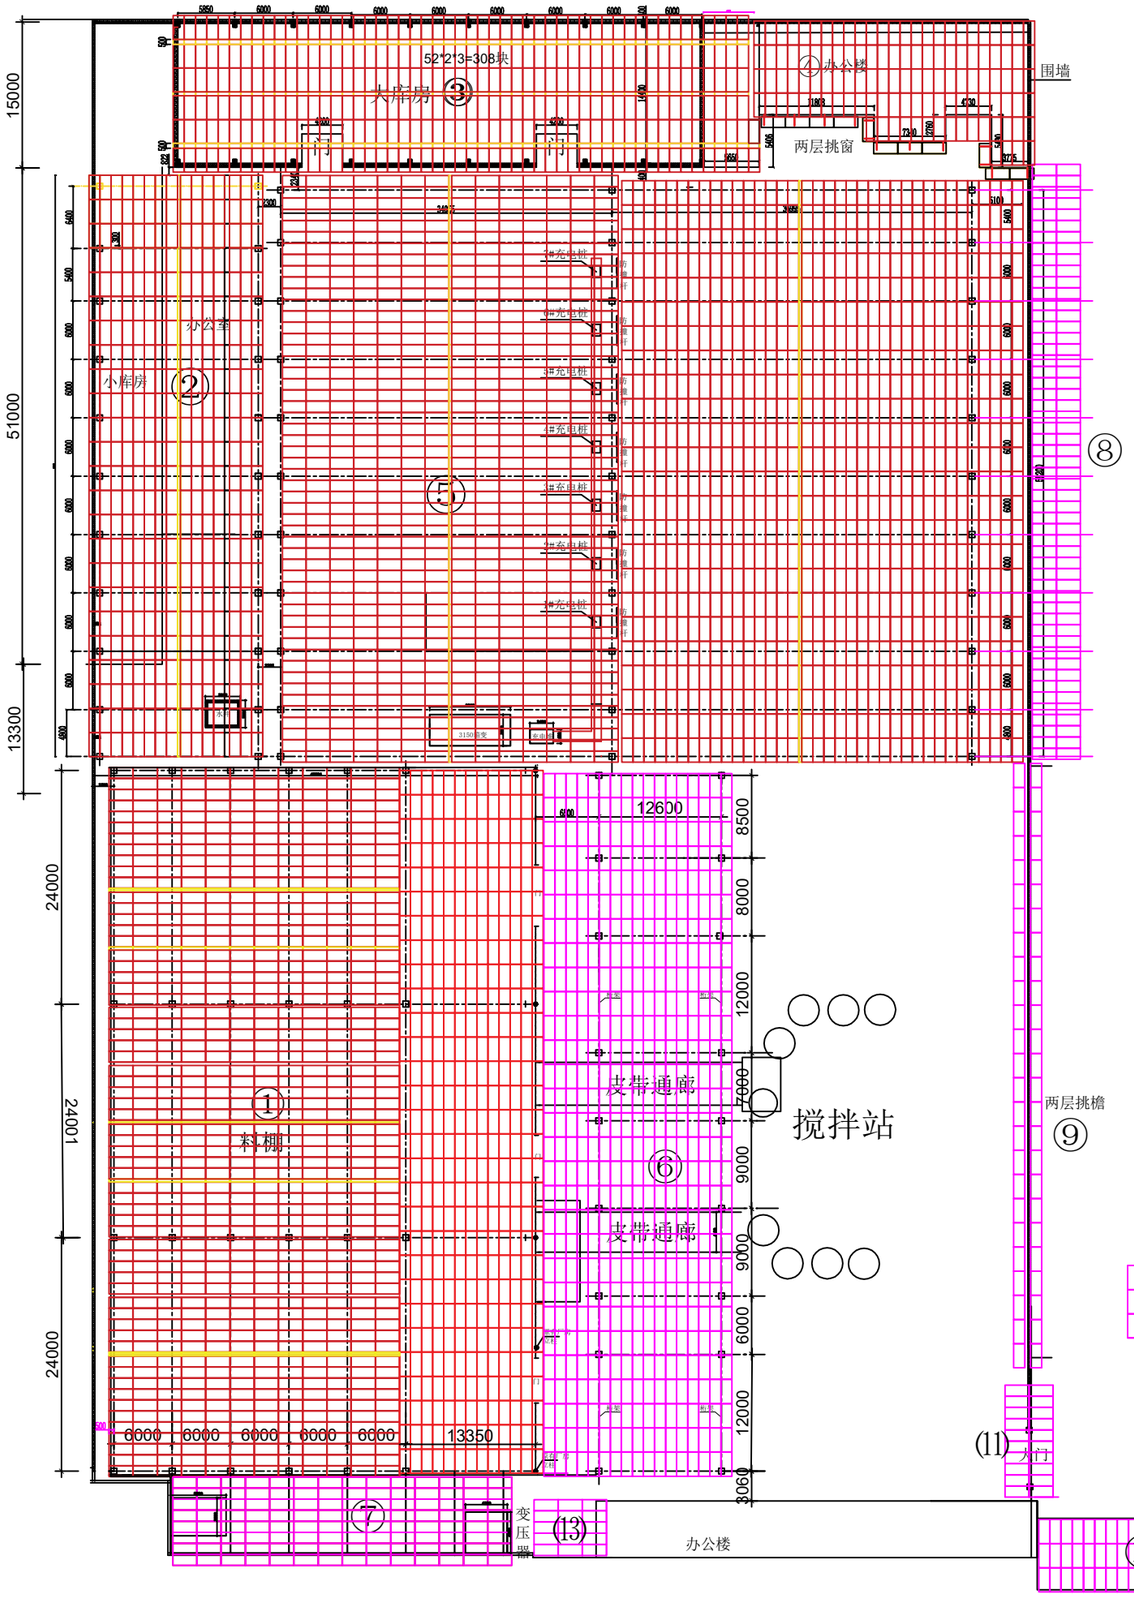


馥裕搅拌站分布式光伏项目光伏板平面布置图

馥裕搅拌站光伏板统计表

序号	项目名称	预估光伏组件数量（块）	容量（kW）	备注
①	三联跨拱形原料棚屋面光伏项目	1121	723.045	
②	小库房屋面光伏项目	360	232.2	
③	大库房屋面及东侧玻璃房光伏项目	308	198.66	
④	办公楼屋面光伏项目+南墙	141	90.945	
⑤	新建二联跨屋面光伏项目	1592	1026.84	
⑥	搅拌站料筒西侧光伏棚	493	317.985	
⑦	原料棚南侧车棚光伏项目	112	72.24	
⑧	食堂及车棚屋面光伏项目	106	68.37	
⑨	东墙光伏支架	100	64.5	
⑩	东大门外侧小车光伏棚	54	34.83	
⑪	东大门门楼上光伏项目	20	12.9	
⑫	东大门外地磅计量室屋面光伏项目	48	30.96	
⑬	配电室屋面光伏项目	15	9.675	
	合计	4470	2883.15	

本文件知识产权属于我公司，未经我们书面许可，不得复制、不得用于本项目之外、不得以任何方式提供给第三方。

山西晋南恒泰新能源科技有限公司

设计		馥裕搅拌站分布式光伏项目光伏板平面布置图		
制图				
审核		图号：		
		日期： 2026.6.29	页次：	第1页，共1页